




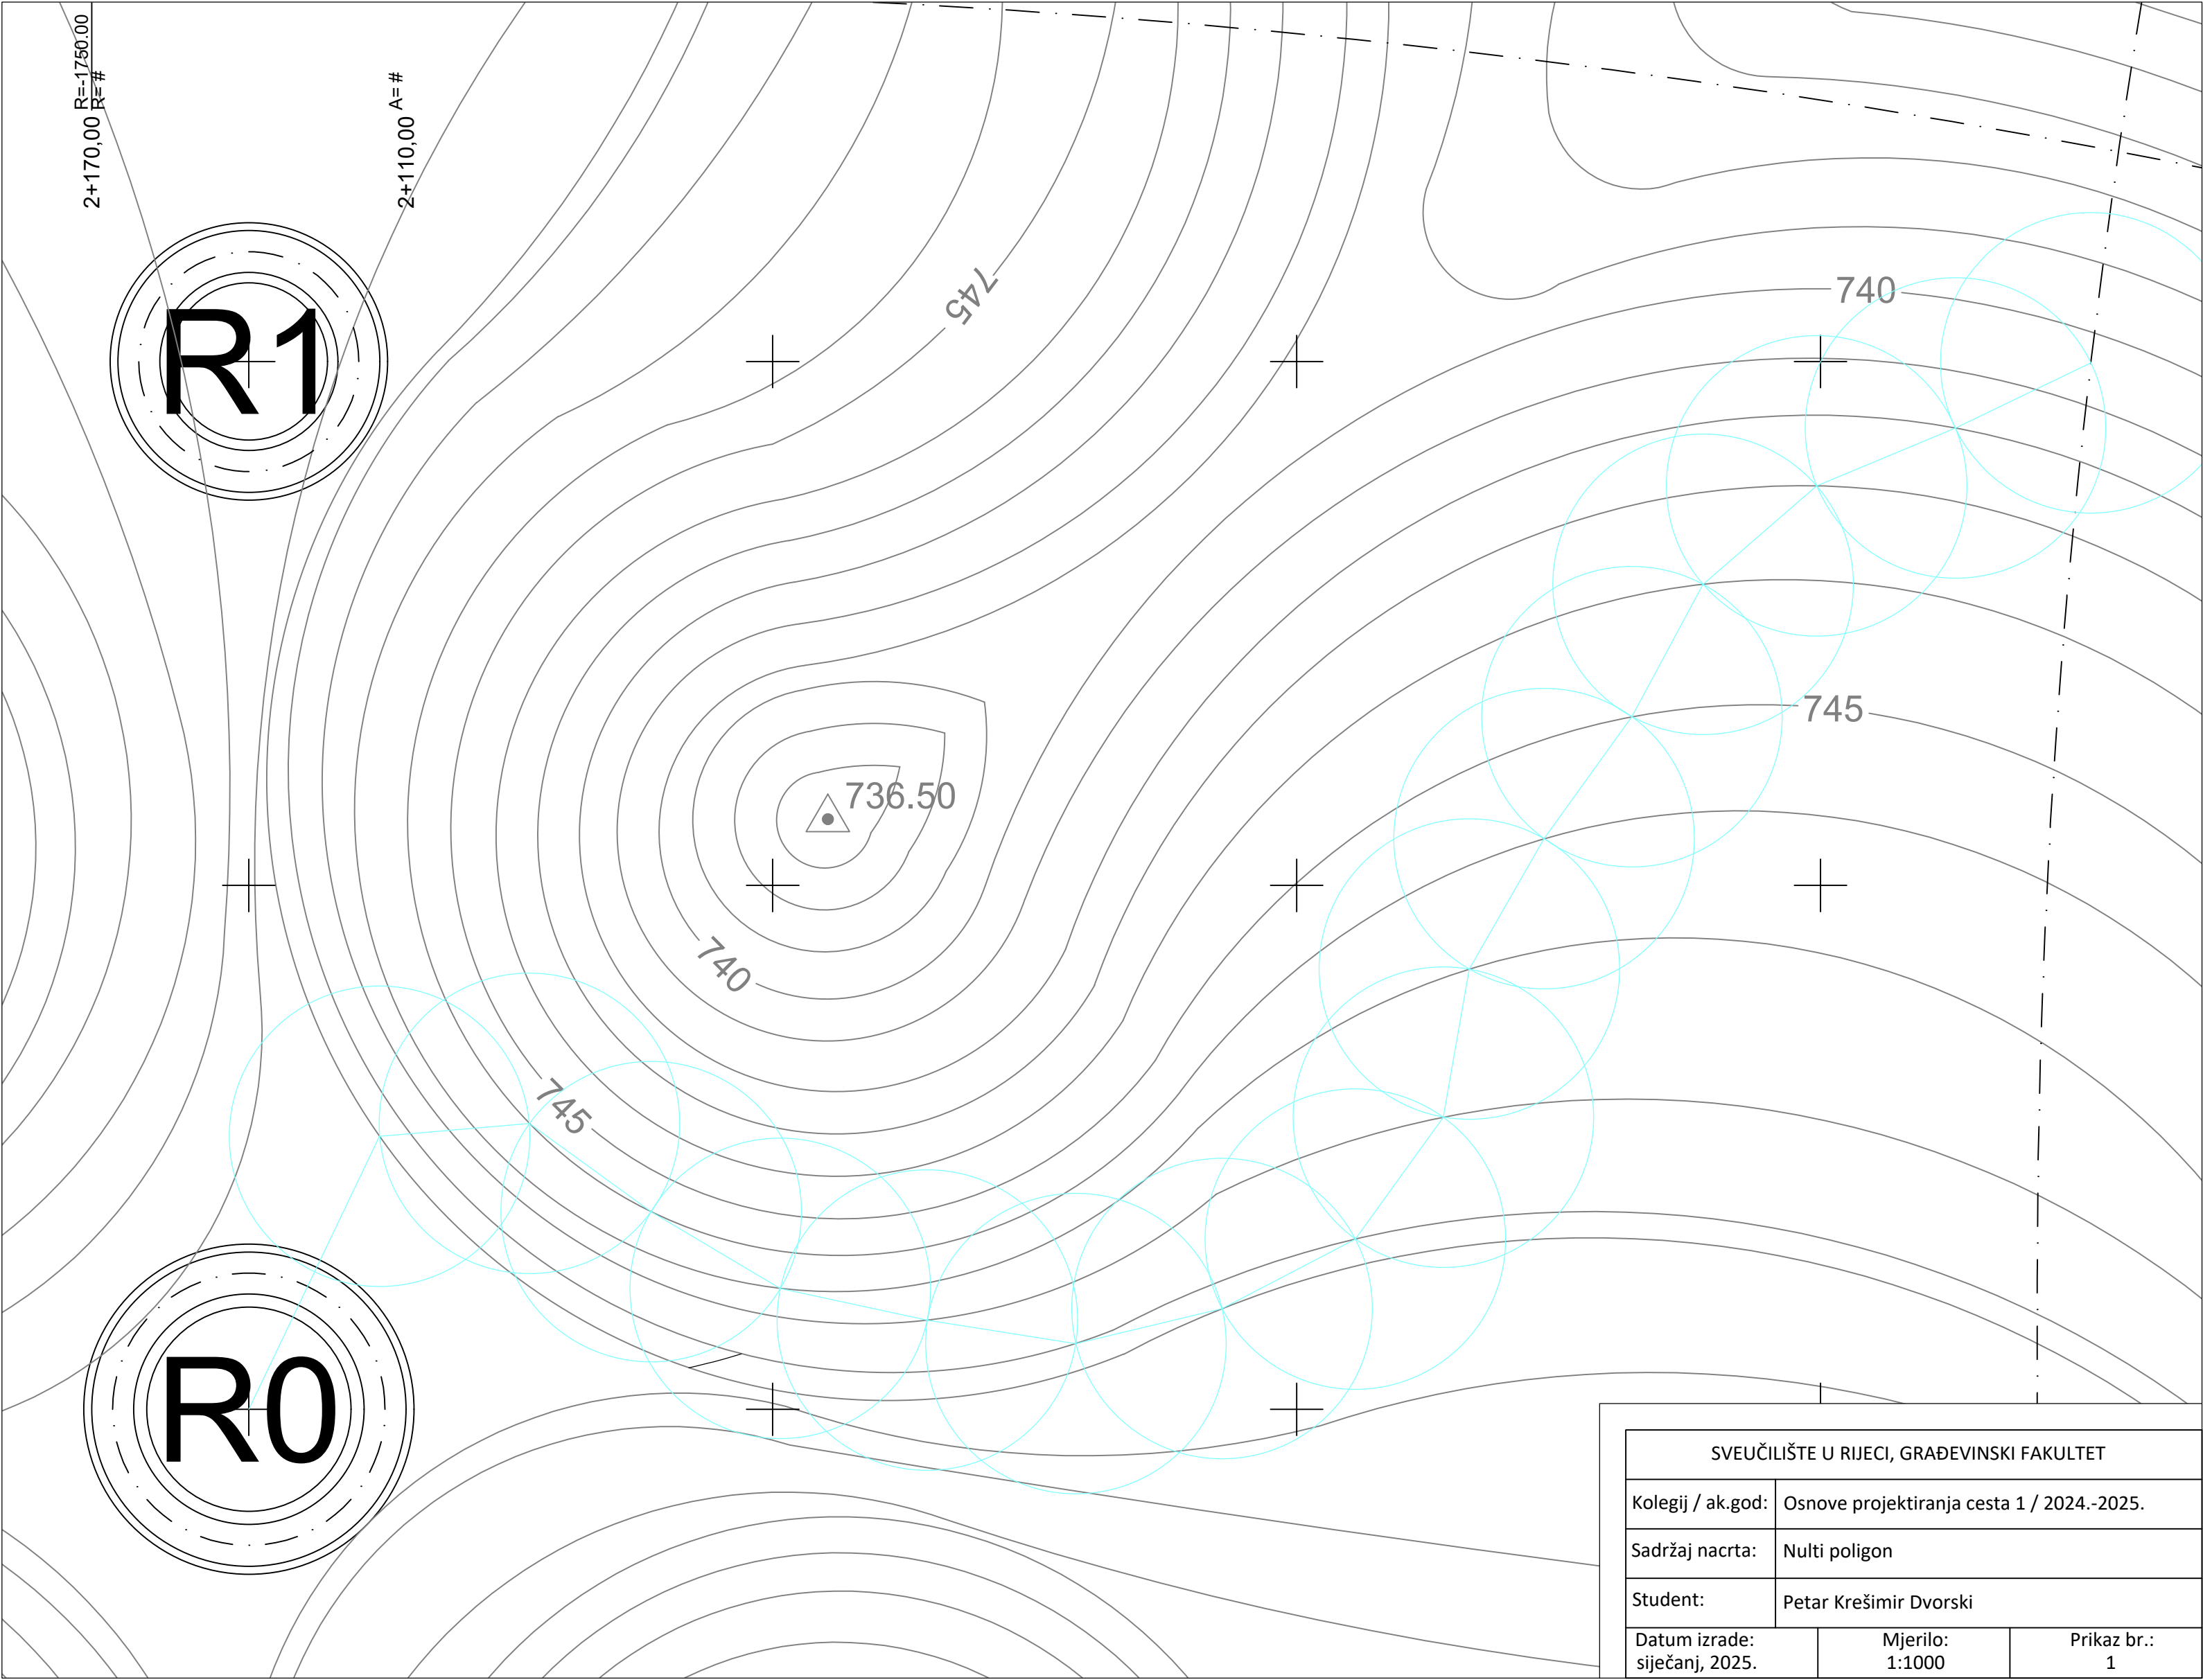

SVEUČILIŠTE U RIJECI, GRAĐEVINSKI FAKULTET		
Kolegij / ak.god:	Osnove projektiranja cesta 1 / 2024.-2025.	
Sadržaj nacrt:	Nulti poligon	
Student:	Petar Krešimir Dvorski	
Datum izrade: siječanj, 2025.	Mjerilo: 1:1000	Prikaz br.: 1

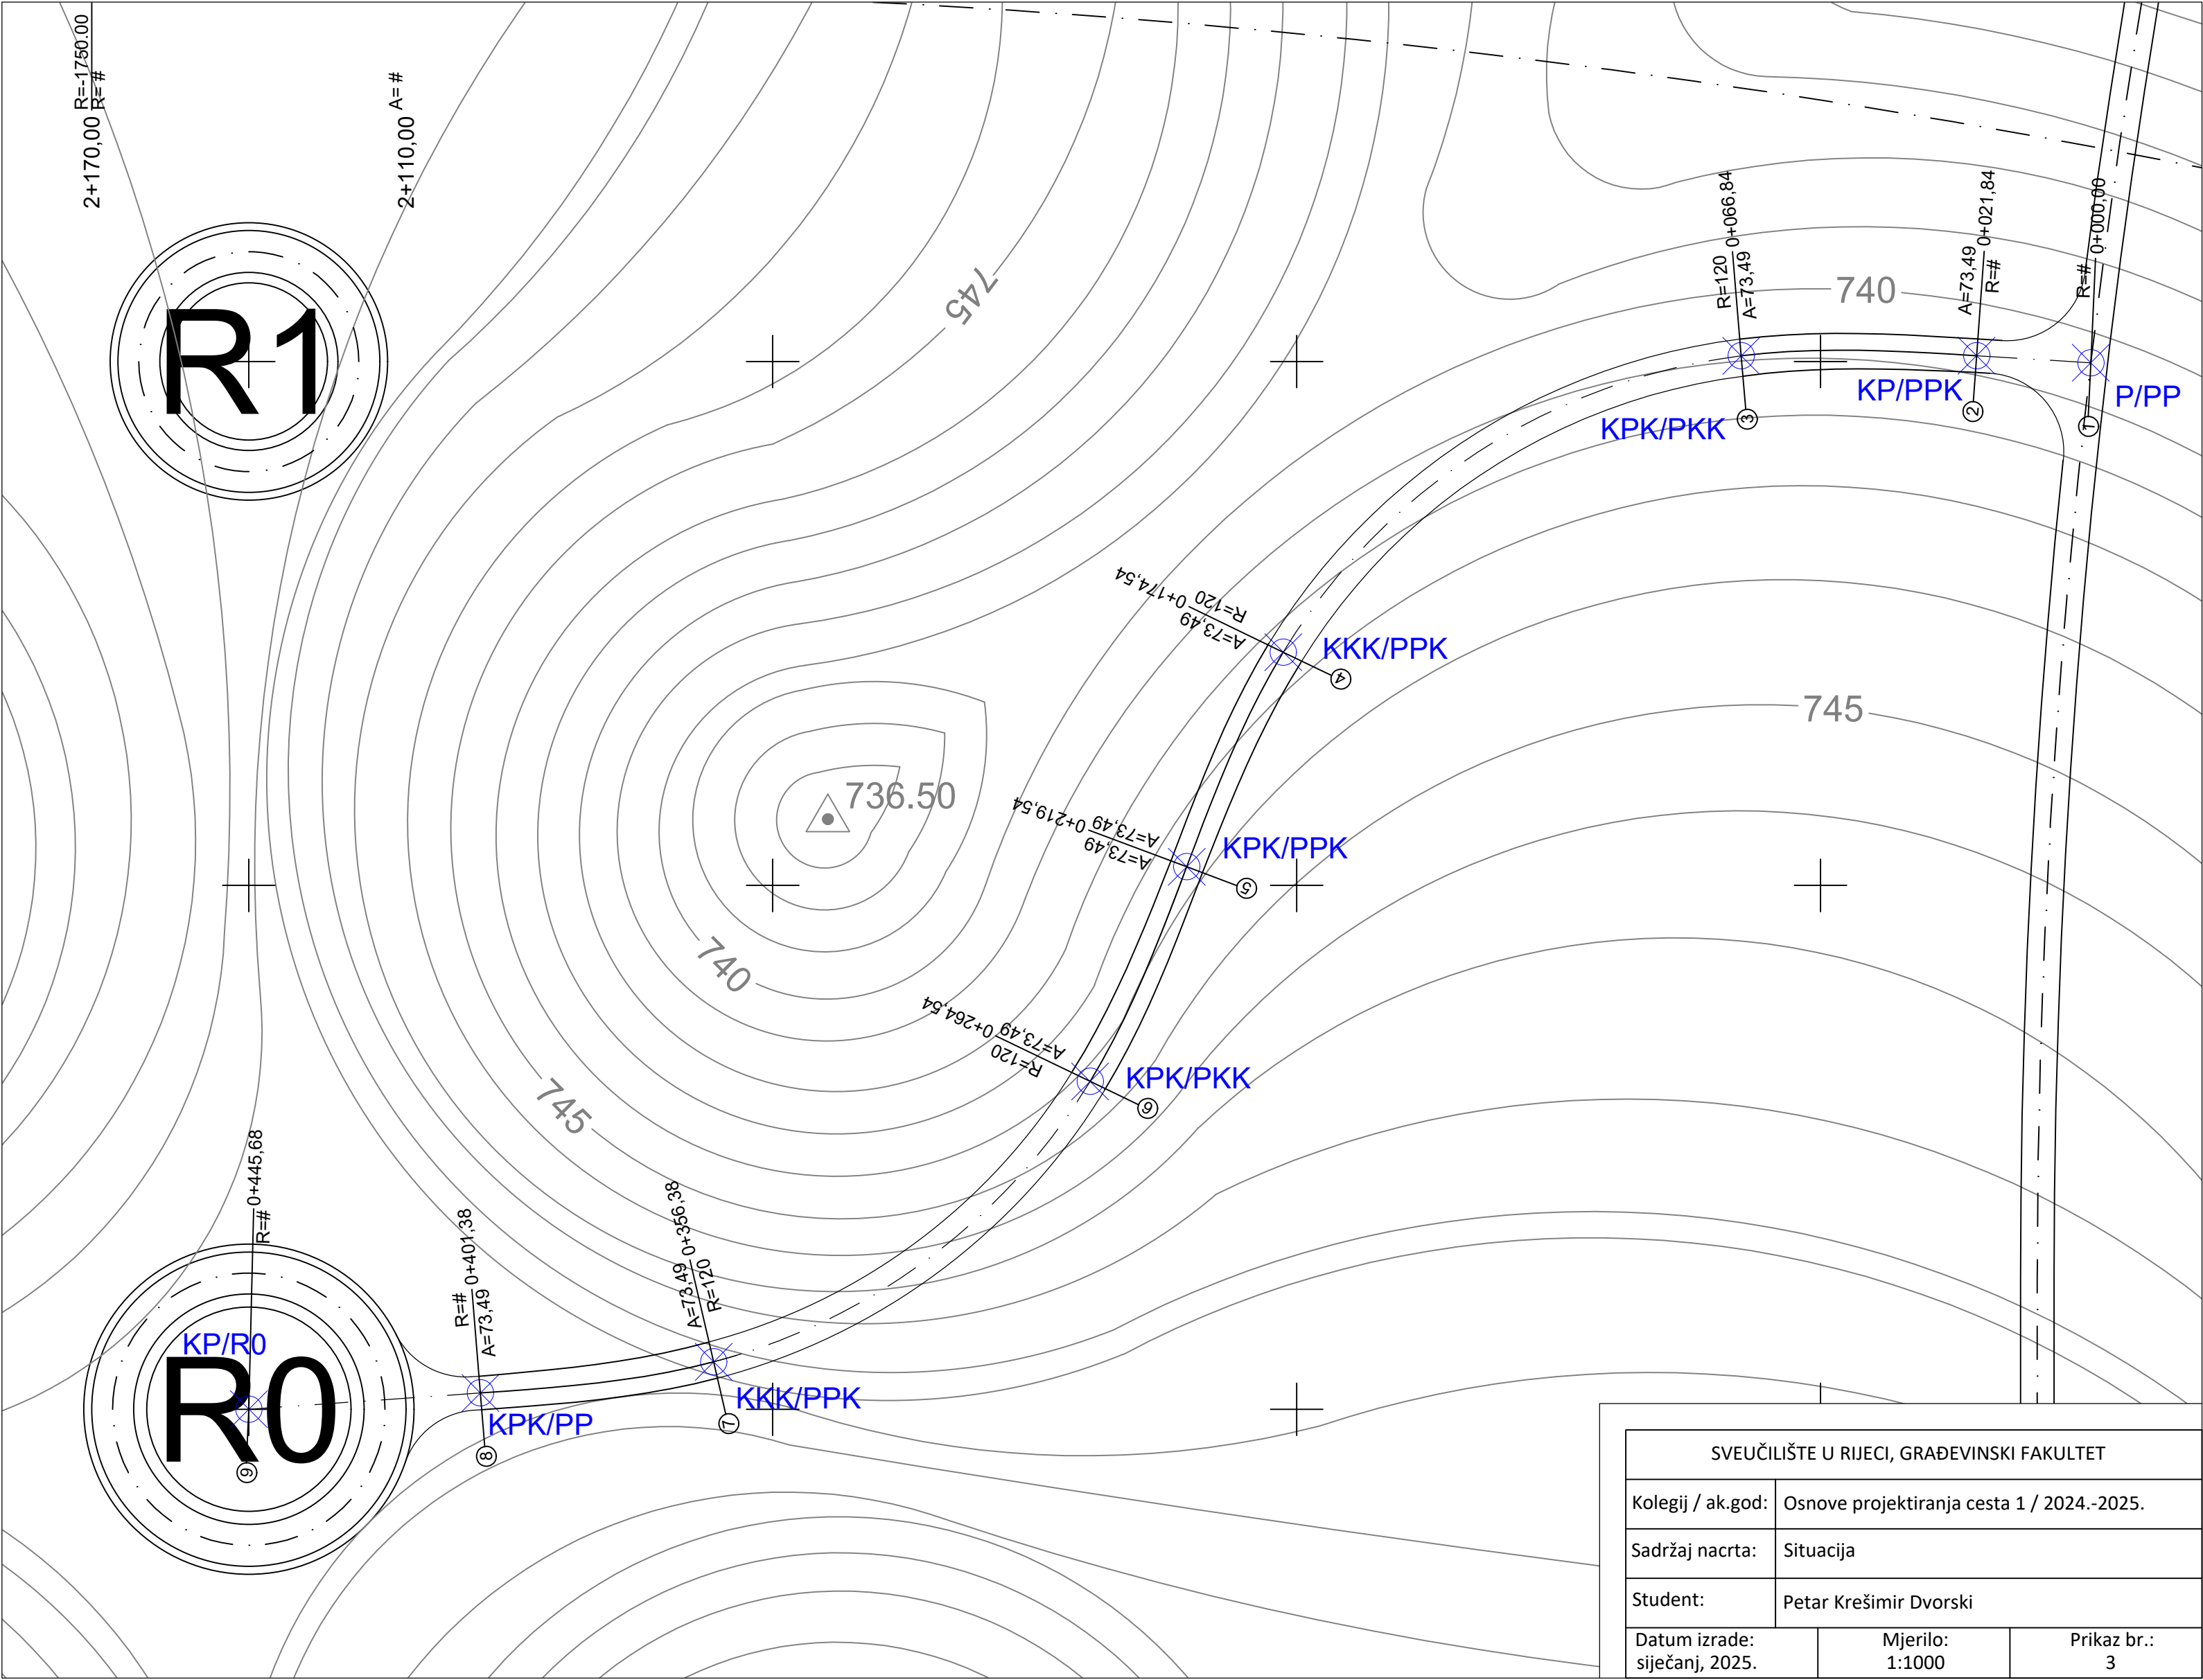


SVEUČILIŠTE U RIJECI, GRAĐEVINSKI FAKULTET		
Kolegij / ak.god:	Osnove projektiranja cesta 1 / 2024.-2025.	
Sadržaj nacrt:	Situacija	
Student:	Petar Krešimir Dvorski	
Datum izrade: siječanj, 2025.	Mjerilo: 1:1000	Prikaz br.: 3

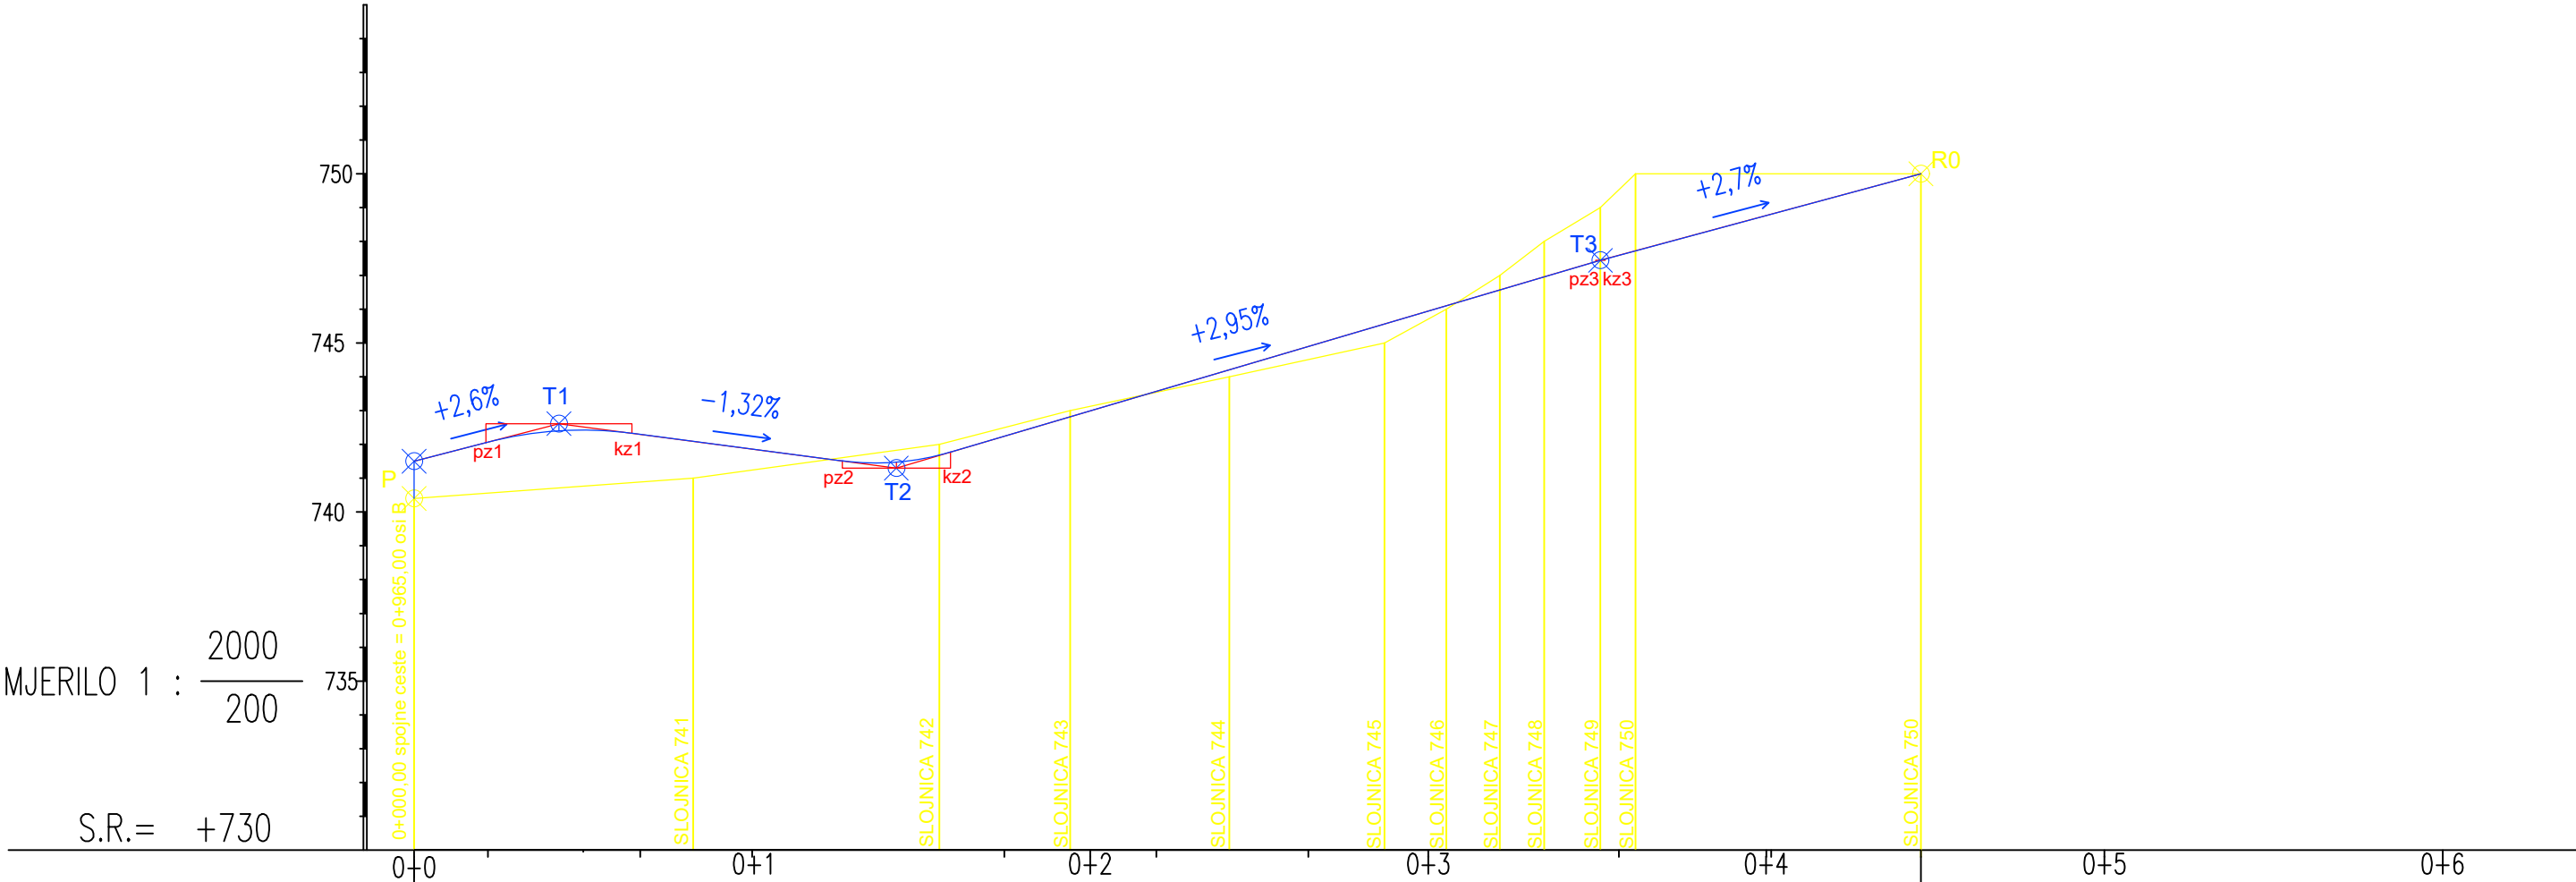

VERTIKALNI TOK	+2,6% l=21,27 Rv=750 l2=16,01 s2=0,17 -1,32% l=62,23 +2,95% l=190,87 Rv=1100 l2=1,38 s2=0,00087 +2,7% l=93,41								
KOTE NIVELETE	1	2	3	4	5	6	7	8	9
KOTE TERENA	-740,40	-740,56	-740,89	-742,50	-743,54	-744,51	-749,53	-748,80	-750
OZNAKA PROFILA	1	2	3	4	5	6	7	8	9
NAGIB KOLNIKA	rozkrižje	rozkrižje	rozkrižje	rozkrižje	rozkrižje	rozkrižje	rozkrižje	rozkrižje	rozkrižje
PROŠIRENJE	L	D	L	D	L	D	L	D	L
VITOPERENJE	rozkrižje	rozkrižje	rozkrižje	rozkrižje	rozkrižje	rozkrižje	rozkrižje	rozkrižje	rozkrižje
HORIZONTALNI TOK	L	D	L	D	L	D	L	D	L
STACIONAŽA	0+000,00	0+019,07 0+021,84	0+066,84	0+174,54	0+219,54	0+264,54	0+356,38	0+402,88 0+404,38	0+445,68

SVEUČILIŠTE U RIJECI, GRAĐEVINSKI FAKULTET		
Kolegij / ak.god:	Osnove projektiranja cesta 1 / 2024.-2025.	
Sadržaj nacрта:	Vertikalni tok	
Student:	Petar Krešimir Dvorski	
Datum izrade: siječanj, 2025.	Mjerilo: 1:1000	Prikaz br.: 4

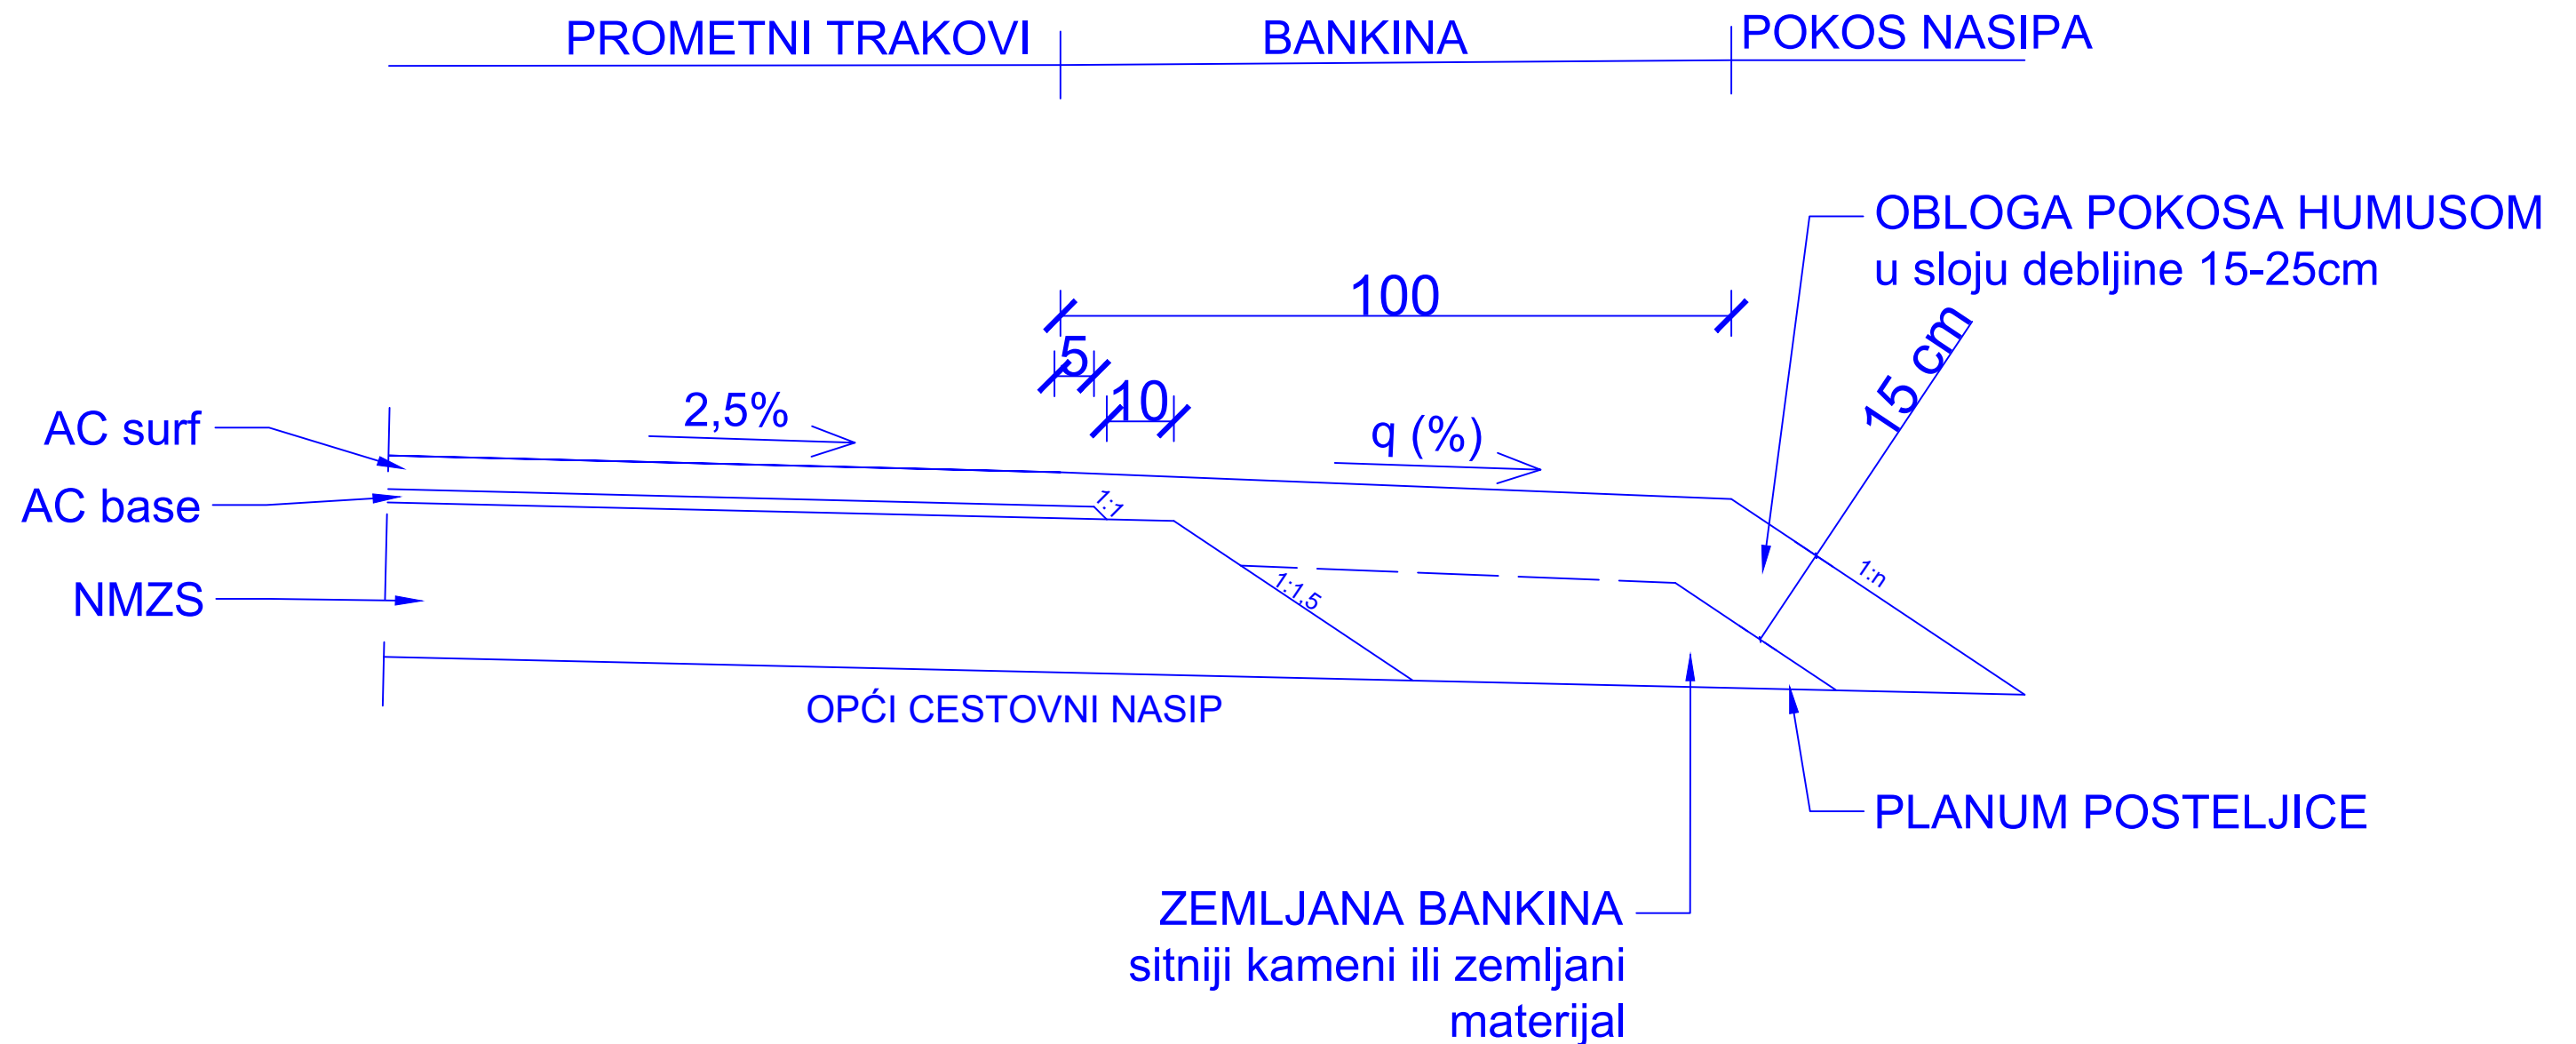

KOLNIČKA KONSTRUKCIJA:

Habajući sloj asfaltbetona AC 11 surf 50/70	5cm
Nosivi sloj asfaltbetona AC 22 base 50/70	7cm
Nosivi sloj nevezanog zrnatog materijala 0-63mm	30cm

SVEUČILIŠTE U RIJECI, GRAĐEVINSKI FAKULTET		
Kolegij / ak.god:	Osnove projektiranja cesta 1 / 2024.-2025.	
Sadržaj nacrt:	Detalj bankine	
Student:	Petar Krešimir Dvorski	
Datum izrade: siječanj, 2025.	Mjerilo: 1:10	Prikaz br.: 5

